

NORTH ELEVATION (SCALE 1/8" = 1'-0")




ELEVATION NOTES

- 1. EXTERIOR WALLS: 8" CMU, GROUTED SOLID; BRICK VENEER ON OFFICE (WEST 100 LF + NORTH 40 LF x 14'-0").
- 2. WAREHOUSE CMU EXPOSED, PAINTED; PARAPET COPING PREFINISHED ALUMINUM 440 LF.
- 3. STOREFRONT: CLEAR ANODIZED ALUMINUM, 1" INSULATED LOW-E GLASS; ENTRANCE 101 PAIR 6'-0" x 7'-0".
- 4. WINDOWS W1: 4'-0" x 5'-0" FIXED ALUMINUM, SILL AT 3'-0" AFF, QTY 10.
- 5. OVERHEAD DOORS OH-1, OH-2: 12'-0" x 14'-0" INSULATED SECTIONAL, MOTOR OPERATED.
- 6. ROOF: TPO, 1/4" PER FT SLOPE TO INTERNAL DRAINS (4) WITH OVERFLOWS (4).


SOUTH ELEVATION



EAST ELEVATION

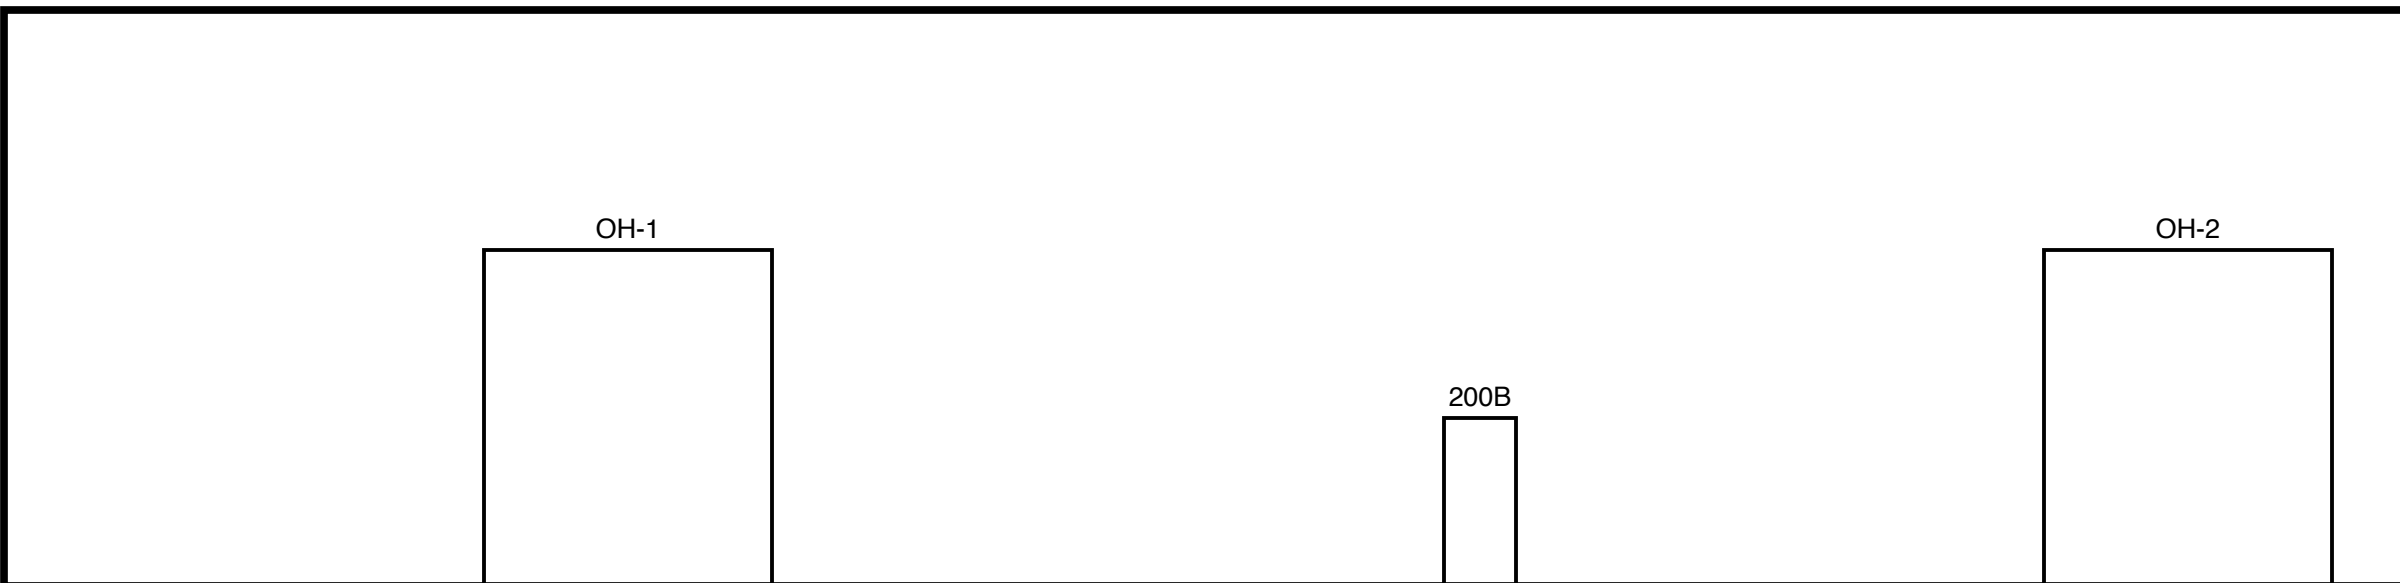

WEST ELEVATION

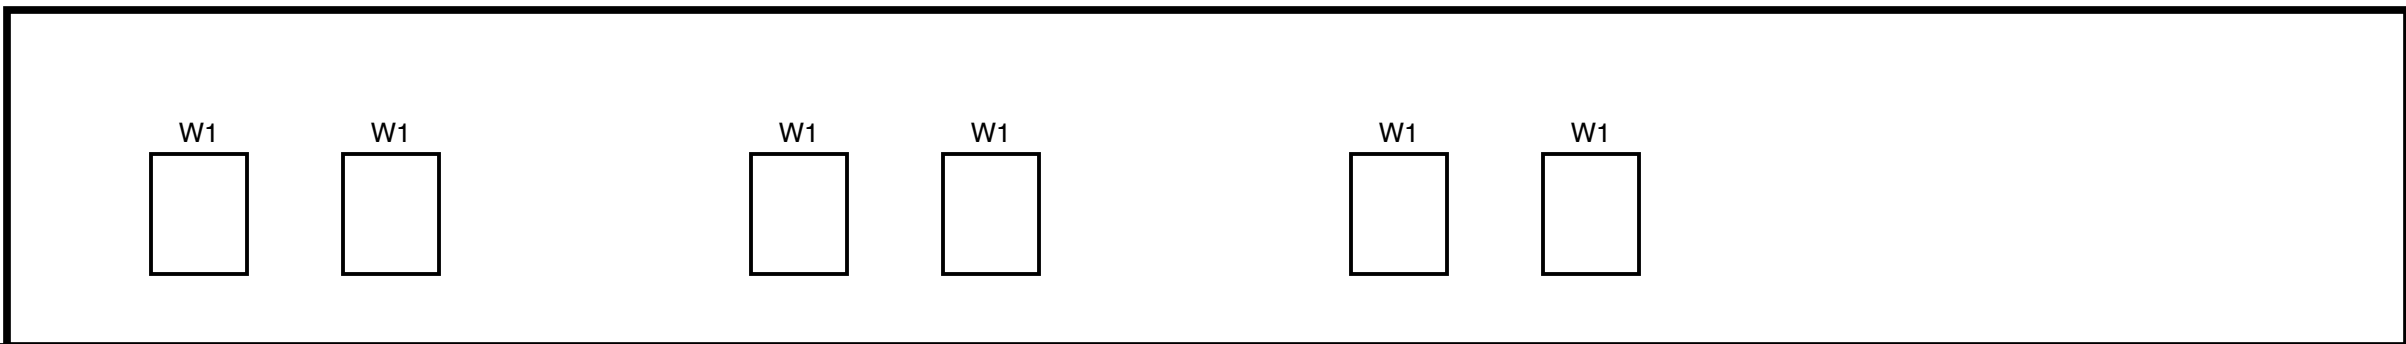

BLACKLAND COMMERCIAL BUILDERS (SYNTHETIC D
PRAIRIE CREEK OFFICE/WAREHOUSE — BUILDING 2

SHEET TITLE
EXTERIOR ELEVATIONS

SCALE: 1/8" = 1'-0" DATE: 09/12/2026
REV: 2 ADDENDUM 1: 09/19/2026

SHEET NUMBER
A-201